



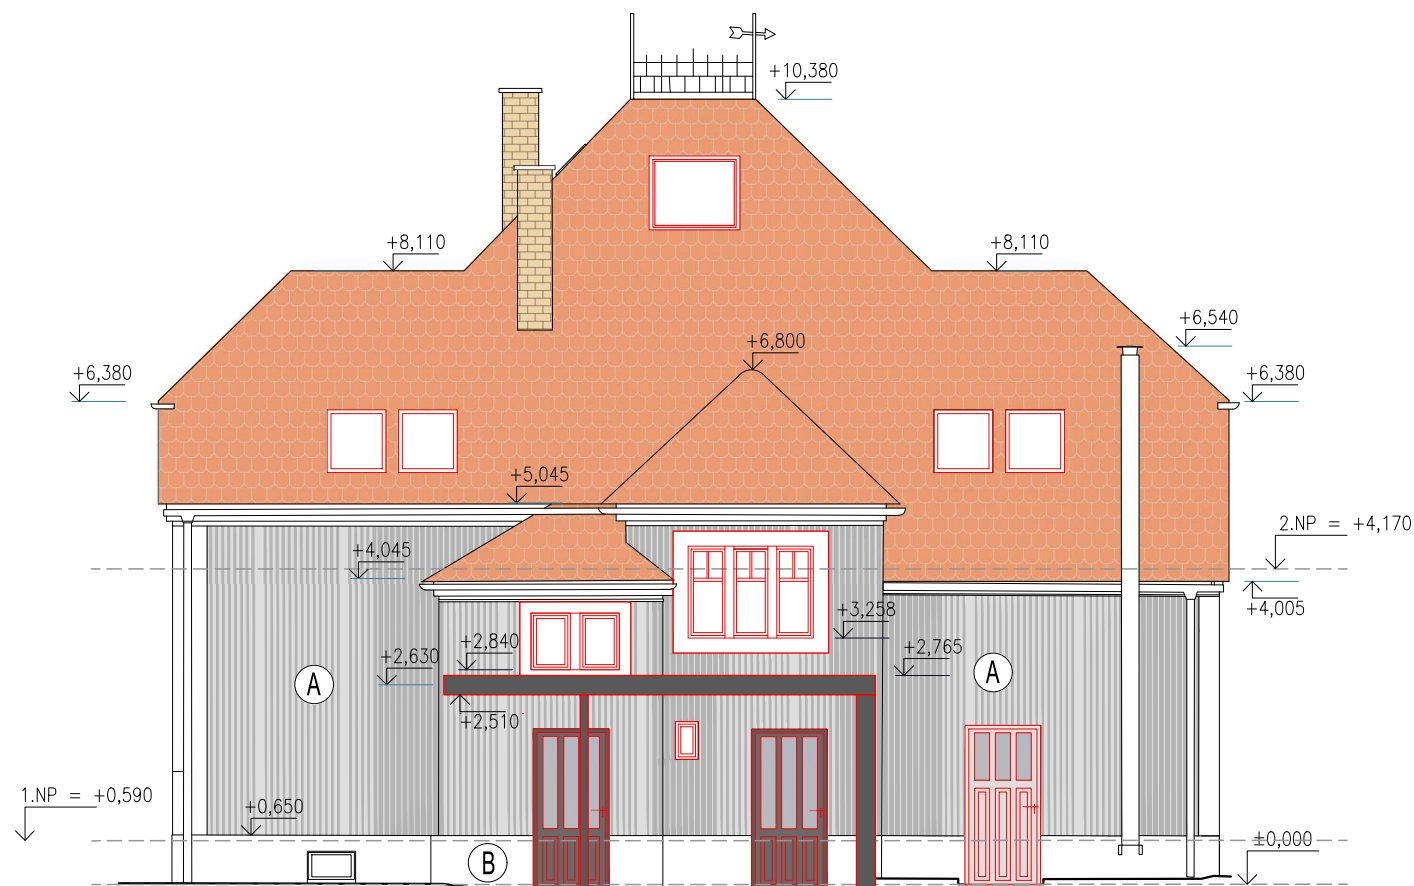

POHLED SZ

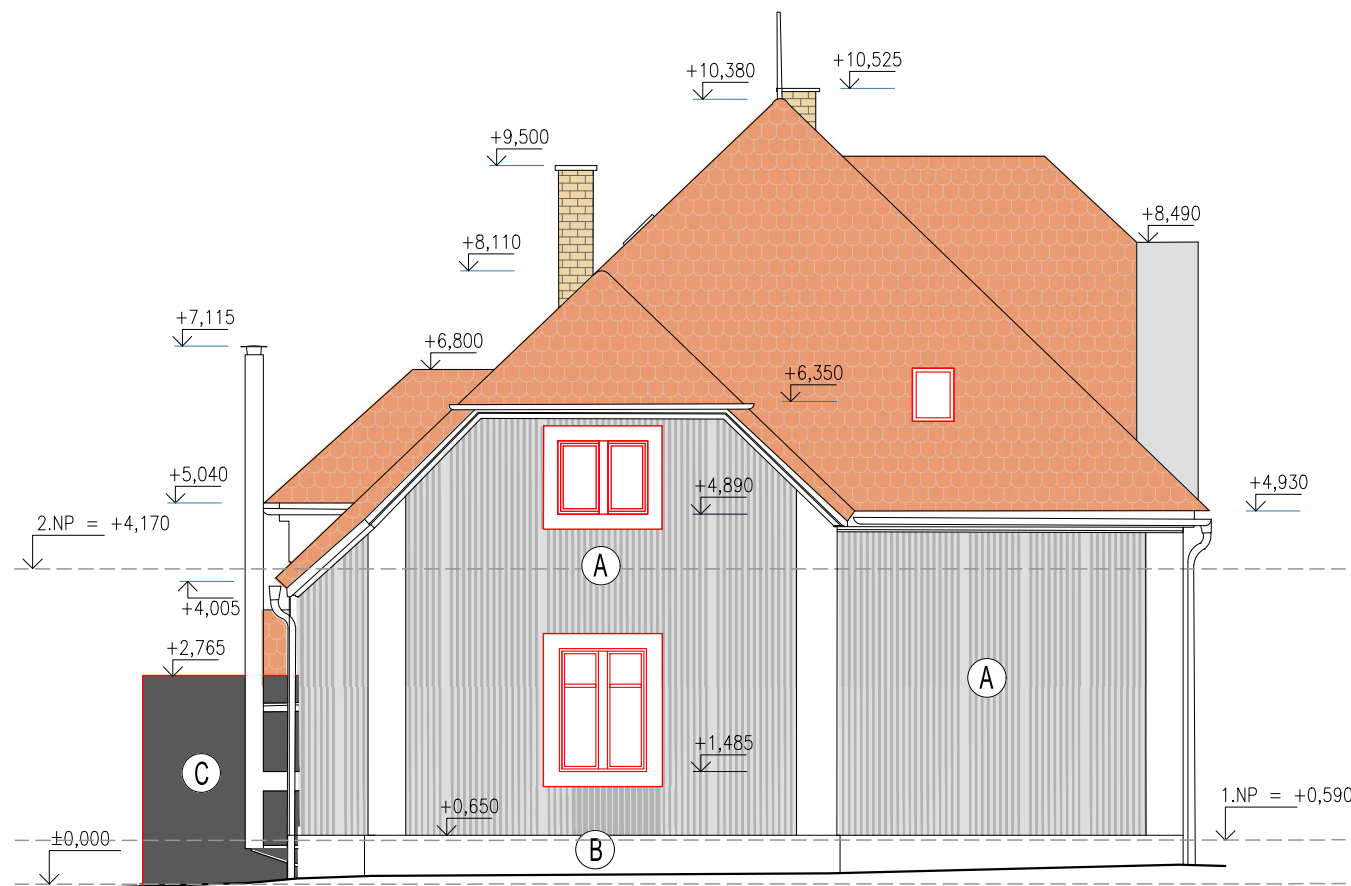

POHLED SV
doupravit

Legenda:

- (A) minerální stěrková hmota (bude upřesněné v rámci AD)
(B) minerální stěrková hmota (bude upřesněné v rámci AD)
— nové konstrukce

±0,000 = 178,000 m.n.m.

INVESTOR

Tobiáš a Zuzana Potočkoví
Mírová 135/57, Litol, 28922 Lysá nad Labem

HLAVNÍ PROJEKTANT

20-20-ARCHITEKTI
MODŘANSKÁ 307/98, 147 00 PRAHA 4
info@2020architekti.cz
+420 603 170 838
2020architekti.cz

AUTOR NÁVRHU

Ing. Šimon Matějovský

STUPEŇ

DPS

DATUM VYDÁNÍ 1. VERZE

03 / 2026

ZODPOVĚDNÝ PROJEKTANT

Ing. arch. Zdeněk Rychtařík

FORMÁT

A3

HIP

Ing. arch. Zdeněk Rychtařík

ZAKÁZKA

204_1

VYPRACOVAL

Filip Turek

MĚŘÍTKO

1:100

ČÍSLO VÝKRESU

D.1.1.18

AKCE

Rekonstrukce rodinného domu

ul. Mírová 135/57, Lysá nad Labem; Litol [689556] p. č. 89/20, st. 138

ČÁST

D.

ARCHITEKTONICKO-STAVEBNÍ

ZPRACOVATEL ČÁSTI

20-20-ARCHITEKTI

MODŘANSKÁ 307/98, 147 00 PRAHA 4
info@2020architekti.cz
+420 603 170 838
2020architekti.cz

NÁZEV VÝKRESU

POHLEDY SZ, SV